

Ведомость основных комплектов рабочих чертежей		
Обозначение	Наименование	Примечание
2604.02082-КЖ0	Конструкции подземной части	
2604.02082-КЖ1	Конструкции надземной части	
2604.02082-КМ	Конструкции металлические	

Ведомость рабочих чертежей основного комплекта марки КЖ1

Лист	Наименование	Примечание
1	Общие данные	
2	Схема расположения вертикальных несущих конструкций на отп. -0,080. Опалубка	
3	Колонна монолитная железобетонная Км-1-1 на отп. -0,080	
4	Колонна монолитная железобетонная Км-1-2 на отп. -0,080	
5	Фрагменты расположения вертикальных несущих конструкций на отп. -0,080. Опалубка	
6	Узлы армирования, типы армирования вертикальных несущих конструкций на отп. -0,080	
7	Спецификация арматуры стен на отп.-0,080. Ведомость деталей	

Ведомость ссылочных и прилагаемых документов		
Обозначение	Наименование	Примечание
	<u>Ссылочные документы</u>	
Серия 1400-15.B1520-06	Унифицированные закладные изделия железобетонных конструкций для крепления технологических коммуникаций и устройств	
ГОСТ 34028-2016	Прокат арматурный свариваемый периодического профиля классов А500С и В500С для армирования железобетонных конструкций. Технические условия	
ГОСТ 26633-2015	Бетоны тяжелые и мелкозернистые. Технические условия	
ГОСТ 3282-74	Проволока стальная низкоуглеродистая общего назначения. Технические условия (с Изменениями N 1-5)	
ГОСТ 8509-93	Уголки стальные горячекатаные равнополочные. Сорбмент	
ГОСТ 27772-2015	Прокат для строительных стальных конструкций. Общие технические условия	
ГОСТ 28013-98	Растворы строительные. Общие технические условия (с Изменением N 1)	
ТУ 5774-003-00287852-99	Материал рулонный кровельный и гидроизоляционный наплаваемым битумно-полимерный водостойкий ТЕХНОЗЛАСТ	
ГОСТ 14098-2014	Соединения сварные арматуры и закладных изделий железобетонных конструкций. Типы, конструкции и размеры	
ТР 186-07	ТЕХНОЛОГИЧЕСКИЙ РЕГЛАМЕНТ на установку гидроизоляционных шпенок АКВАСТОП при устройстве и восстановлении гидроизоляций деформационных технологических швов бетонирования в железобетонных конструкциях подземных и заглубленных сооружений	
ТК	ТЕХНОЛОГИЧЕСКАЯ КАРТА на устройство гидроизоляции фундаментов методом наплавления с применением рулонного битумно-полимерного материала Технозласт ЭПП	
ТУ 5775-011-17925162-2003	Битумный концентрат "Праймер"	
	<u>Прилагаемых документов нет</u>	

Ведомость спецификаций

Лист	Наименование	Примечание
3	Спецификация арматуры Кн-1-1	
4	Спецификация арматуры Кн-1-2	
7	Спецификация арматуры стен на оп. -0,080	

Ведомость расхода бетона, м³

Конструкция	Бетон класса		
	ГОСТ 26633-2015		
	B25	B30	Итого
Колонны монолитные на опм. -0,080	0	75,66	75,66
Стены монолитные на опм. -0,080	269,32	0	269,32
Всего	269,32	75,66	344,98

Ведомость расхода стали, кг

Марка конструкции	Изделия арматурные										Всего
	Арматура класса										
	A240			A500С							
	ГОСТ 34028-2016			ГОСТ 34028-2016							
	Ø8	Ø10	Итого	Ø10	Ø12	Ø16	Ø32	Итого			
Колонны монолитные на отм.-0,080	0	1710,9	1710,9	0	0	0	24533,3	24533,3	26244,2		
Стены монолитные на отм. -0,080	1732,1	1732,1	1732,1	9450,8	13077,8	1485,3	0	24013,9	25746		
Общий расход	1732,1	1710,9	3443	9450,8	13077,8	1485,3	24533,3	48547,2	51990,2		

ОБЩИЕ УКАЗАНИЯ

ОБЩИЕ ПОЛОЖЕНИЯ

1. Настоящая рабочая документация для строительства объекта «Лабораторно-производственный корпус», расположенного по адресу: г. Москва, г. Зеленоград, проспект Генерала Алексеева, 50Б, разработана на основании:

- задания на проектирование, утвержденного Заказчиком;
- рабочих чертежей марки АР;
- задания от смежных разделов рабочей документации;
- технического отчёта по результатам инженерно-геологических изысканий, выполненного ООО «ЭККЕР» в июне 2026 года, шифр: 1205_КИИ-ИГИ;
- результатов инженерно-геодезических изысканий, выполненных ООО «ЭККЕР» в 2026 году;
- иных исходных данных, переданных Заказчиком.

2. Классификация объекта капитального строительства по назначению и функционально-технологическим особенностям в соответствии с приказом Министра России от 02.11.2022 № 928/пр:

- код объекта: 08.03.05.01;
- наименование объекта: лечебно-производственный корпус.

3. Рабочие чертежи разработаны с соблюдением требований:

- Федерального закона от 30.12.2009 № 384-ФЗ «Технический регламент о безопасности зданий и сооружений»;
- Федерального закона от 22.07.2008 № 123-ФЗ «Технический регламент о требованиях пожарной безопасности»;
- ГОСТ Р 21.101.2026 «Система проектной документации для строительства. Основные требования к проектной и рабочей документации и конструктивным решениям»;
- ГОСТ Р 51.501.2018 «Система проектной документации для строительства. Правила выполнения рабочей документации архитектурных и конструктивных решений»;
- СП 20.13330.2016 «Нагрузки и воздействия»;
- СП 22.13330.2016 «Основания зданий и сооружений»;
- СП 63.13330.2018 «Бетонные и железобетонные конструкции. Основные положения»;
- СП 16.13330.2017 «Стальные конструкции»;
- СП 381.1325800.2018 «Сооружения подпорные. Правила проектирования»;
- СП 305.1325800.2017 «Здания и сооружения. Правила проведения геотехнического мониторинга при строительстве»;
- СП 28.13330.2017 «Защита строительных конструкций от коррозии»;
- СП 48.13330.2019 «Организация строительства»;
- СП 45.13330.2017 «Земляные сооружения, основания и фундаменты»;
- СП 70.13330.2012 «Несущие и ограждающие конструкции»;
- СП 71.13330.2017 «Изоляционные и отделочные покрытия»;
- СП 126.13330.2017 «Геодезические работы в строительстве»;
- ГОСТ Р 51872-2024 «Документация исполнительная геодезическая. Правила выполнения»;
- ГОСТ 34329-2016 «Опалубка. Общие технические условия»;
- ГОСТ 34029-2016 «Прокладки арматурные для железобетонных конструкций. Технические условия»;
- ГОСТ 7473-2019 «Смеси бетонные. Технические условия»;
- ГОСТ 26633-2015 «Бетоны тяжёлые и мелкозернистые. Технические условия»;
- ГОСТ 18105-2018 «Бетоны. Правила контроля и оценки прочности».

4. За относительноную отметку 0,000 принят уровень чистого пола первого этажа, соответствующий абсолютной отметке 224,35 в принятой системе высот.
5. Система высот — Московская. Система геодезических координат — Московская.
6. Все размеры на чертежах приведены в миллиметрах, отметки — в метрах, если на чертеже не указано иное.
7. Размеры и отметки определять только по значениям, указанным на чертежах. Определение размеров измерением по чертежам не допускается.
8. Настоящий комплект рассматривать совместно с рабочими чертежами марок АР, ГП, КЖ других комплектов, а также с чертежами наружных и внутренних инженерных систем.
9. Работы выполнять по согласованному проекту производства работ, технологическим картам и программе геотехнического мониторинга.
10. До начала работ строительной организации необходимо:
 - вынести и закрепить основные оси здания и границы котлована;
 - выполнить начальный цикл геотехнического мониторинга;
 - разработать ППР.
11. Замена предусмотренных проектом материалов, изделий, классов бетона и арматуры, изменение размеров и положения конструкций, отверстий, закладных изделий, рабочих швов и технологической последовательности допускаются только по согласованию с проектной организацией.
12. Все применяемые материалы и изделия должны иметь документы о качестве, подтверждающие соответствие требованиям рабочей документации и нормативных документов.
13. Рабочая документация разработана в соответствии с заданием на проектирование, утверждённой проектной документацией, техническими условиями и требованиями действующих технических регламентов, стандартов и сводов правил и обеспечивает безопасную эксплуатацию объекта при соблюдении предусмотренных проектом решений и правил производства работ.

ОБЩИЕ ТРЕБОВАНИЯ К МОНОЛИТНЫМ ЖЕЛЕЗОБЕТОННЫМ КОНСТРУКЦИЯМ

14. Классы бетона по прочности, марки по водонепроницаемости и морозостойкости, классы и диаметры арматуры, толщину защитного слоя, расположение рабочих швов, выпусков, закладных изделий и технологических отверстий принимать по рабочим чертежам.
15. Устройство стен, колонн и перекрытия выполнять в соответствии с рабочими чертежами, утверждённым ППР, технологическими картами и требованиями СП 63.13330.2018, СП 70.13330.2012 и СП 435.1325800.2018.
16. Перед началом работ выполнить геодезическую разбивку осей, переподать отметок, граний стен и колонн, отметок низа и верха технологических проёмов, закладных изделий, выпусков арматуры и зон displacement армирования.
17. Опалубку стен, колонн и перекрытия устанавливать по утверждённой схеме, обеспечивающей проектное положение конструкций, геометрическую неизменяемость, прочность, жёсткость и устойчивость на всех стадиях бетонирования.
18. До начала армирования опалубку очистить от мусора, льда, масла и иных загрязнений. Поверхности опалубки, соприкасающиеся с бетоном, подготовить в соответствии с принятой технологией.
19. До бетонирования проверить проектное положение опалубки, арматуры, закладных изделий, гильз, технологических отверстий, выпусков инженерных коммуникаций и элементов заземления.
20. Армирование стен, колонн и перекрытия выполнять в строгом соответствии с рабочими чертежами. Изменение диаметра, класса, шага, количества и положения арматуры без согласования с проектной организацией не допускается.
21. Арматуру до установки защищать от загрязнения, коррозионного повреждения и механических воздействий. Перед бетонированием удалить с арматуры лёд, масло, грязь и отслаивающиеся продукты коррозии.
22. Проектную толщину защитного слоя бетона обеспечивать инвентарными фиксаторами. Применение обрезков арматуры, древесины, кирпича, щебня и иных случайных предметов в качестве фиксаторов не допускается.
23. Работы по устройству арматуры, длины анкеров, перепалы, а также взаимное расположение стыков выполнять по рабочим чертежам. Устройство неполноценных стыков без согласования с проектной организацией не допускается.
24. Сварку и привкутку арматуры выполнять только в случаях, предусмотренных рабочими чертежами и технологией производства работ.
25. Арматурные стыки, каркасы и отдельные стержни закреплять так, чтобы их проектное положение сохранялось при перемещении рабочих, установке закладных деталей, подаче и уплотнении бетонной смеси.
26. Закладные изделия, анкеры, гильзы, проходы, выпуски арматуры и элементы инженерных систем установить и закрепить до бетонирования, исключив их смещение при укладке бетонной смеси.
27. Устройство не предусмотренных рабочими чертежами отверстий, штраб и проходов, а также вырезание, сверление или отгиб рабочей арматуры не допускается.
28. Расположение рабочих швов бетонирования стен, колонн и перекрытия принимать по рабочим чертежам и ППР. Устройство непредусмотренных рабочих швов допускается только после согласования с проектной организацией.
29. Бетонную смесь применять заводского изготовления. Состав смеси должен обеспечивать проектные показатели бетона, требуемую удобоукладываемость, однородность и долговечность конструкций.
30. Бетонную смесь укладывать в последовательности и слоями, предусмотренными ППР, исключая расслоение смеси и смещение арматуры, закладных изделий, проходов и опалубки.
31. Уплотнение бетонной смеси выполнять вибраторами соответствующего типа. Режим уплотнения должен исключать образование раковин и пустот, расслоение смеси, повреждение опалубки и смещение арматуры, в том числе каркасов от проваливания.
32. Перед продолжением бетонирования поверхность рабочего шва очистить от цементного молока, слабого бетона и загрязнений и подготовить в соответствии с ППР.
33. После укладки бетона обеспечить температурно-усадочный уход, исключая преждевременное высыхание, промерзание, перегрев и образование температурно-усадочных трещин.

ЗАЩИТА СТАЛЬНЫХ ИЗДЕЛИЙ ОТ КОРРОЗИИ

34. Антикоррозионную защиту стальных конструкций и открытых поверхностей закладных изделий выполнять в соответствии с рабочими чертежами и требованиями СП 28.13330.2017.

35. Поверхности закладных изделий, предназначенные для сцепления с бетоном, окрашивать не допускается.

36. Покрытие участков стальных изделий, повреждённое при транспортировании, монтаже или сварке, восстановить материалами, совместимыми с проектной системой антикоррозионной защиты.

МОНОЛИТНЫЕ ЖЕЛЕЗОБЕТОННЫЕ СТЕНЫ

37. Вертикальную и горизонтальную арматуру стен, соединительные элементы, дистанционные фиксаторы и граничные каркасы устанавливать с соблюдением проектного шага и положения относительно грани конструкции.

38. Дополнительное армирование у проёмов, углов, пересечений стен, мест изменения толщины и примыканий выполнять по рабочим чертежам. Сращивание или исключение отдельных стержней из-за проходок и закладных изделий не допускается.

39. При бетонировании стен учитывать давление бетонной смеси на опалубку. Скорость подъёма уровня смеси назначать ППР с учётом расчётной несущей способности опалубки и температуры бетонной смеси.

МОНОЛИТНЫЕ ЖЕЛЕЗОБЕТОННЫЕ КОЛОННЫ

40. Продольную и поперечную арматуру колонн, хомуты, шпильки и фиксаторы устанавливать в проектном положении. Шаг поперечной арматуры в приопорных зонах и местах стыков продольных стержней принимать строго по рабочим чертежам.

41. Рабочие швы колонн, а также армирование узлов их сопряжения с перекрытием выполнять в местах и по решениям, указанным в рабочих чертежах.

41. Рабочие швы колонн, а также армирование узлов их сопряжения с перекрытием выполнять в местах и по решениям, указанным в рабочих чертежах.

47. Габариты швы колонн, а также армирование узлов их сопряжения с перекрытием выполнять в местах и по решениям, указанным в рабочих чертежах.

МОНОЛИТИЧНОЕ ЖЕЛЕЗОБЕТОННОЕ ПЕРЕКРЫТИЕ

42. Опалубку и стойки перекрытия устанавливать по расчётной схеме ППР. Основание под стойки должно исключать их осадку и потерю устойчивости; удаление или перестановка стоек без разрешения ответственного производителя работ не допускается.

43. Нижнюю и верхнюю арматуру перекрытия, опорные и пролётные стержни, поддерживающие каркасы и фиксаторы устанавливать в проектное положение. Верхняя арматура должна сохранять проектную отметку при бетонировании.

44. Каркасы поперечного армирования от продавливания устанавливать строго по рабочим чертежам: с соблюдением привязки к осям и граням колонн, ориентации, размеров, отметок, расстояний от граней колонн и взаимного шага элементов.

45. Каркасы от продавливания надёжно закреплять к основной арматуре перекрытия до бетонирования. Их смещение, разворот, изменение высотного положения, подрезка либо замена отдельных элементов без согласования с проектной организацией не допускается.

46. До бетонирования перекрытия выполнить инструментальную проверку фактического положения каркасов от продавливания. Результаты проверки зафиксировать в исполнительной документации и предъявить при освидетельствовании армирования до его закрытия последующими работами.

47. Перекрытия выполнять непрерывно в пределах принятой захватки с равномерной укладкой и уплотнением бетонной смеси. Складирование смеси кучами, вызывающее перегрузку опалубки и смещение верхней арматуры, не допускается.

48. Распалубку, удаление или перестановку стоек, приложение строительных нагрузок и складирование материалов на перекрытия выполнять после достижения бетоном прочности, установленной рабочими чертежами и ППР.

КОНТРОЛЬ КАЧЕСТВА И ИСПОЛНИТЕЛЬНАЯ ДОКУМЕНТАЦИЯ

49. В процессе строительства выполнять входной, операционный и приёмочный контроль материалов, изделий и выполненных работ.

50. Прибегать к исполнительной документации оформлять в соответствии с действующими нормативными требованиями и ППР.

51. Осуществлять до закрытия последующими работами следующие задачи:

- опалубка стен, колонн и перекрытия, включая станы и элементы её крепления;
- армирование стен, включая дополнительное армирование проёмов, углов, пересечений и примыканий;
- армирование колонн, включая поперечную арматуру и зоны стыков продольных стержней;
- нижнее и верхнее армирование перекрытия, поддерживающие каркасы и фиксаторы;
- каркасы поперечного армирования перекрытия от продавливания;
- закладные изделия, гильзы, выпуски, отверстия и проходы;
- подготовленные рабочие швы стен, колонн и перекрытий.

52. При выполнении работ, контроль которых будет невозможен после выполнения последующих работ.

53. До бетонирования стен проверить и освидетельствовать положение осей и граней, толщину стен, отметки, размеры и положение проёмов, закладных изделий и проходов, класс, диаметр и шаг вертикальной и горизонтальной арматуры, дополнительное армирование у проёмов, углов, пересечений и примыканий, длины анкеровки и перепуска, толщину защитного слоя, чистоту, геометрию и устойчивость опалубки.

54. До бетонирования колонн проверить и освидетельствовать положение осей, размеры сечения и вертикальность стоек, класс, диаметр и положение продольной арматуры, шаг хомутов и шпилек, армирование зон стыков и сопряжений, длины анкеровки и перепуска, толщину защитного слоя, положение закладных изделий и подготовку рабочего шва.

55. До бетонирования перекрытия проверить и освидетельствовать отметки и геометрию опалубки, расчётную схему и устойчивость стоек, положение нижней и верхней арматуры, опорных и пролётных стержней, поддерживающих каркасы и фиксаторов, толщину защитного слоя, положение проёмов, закладных изделий, гильз и проходов, а также чистоту опалубки.

56. Положение каркасов поперечного армирования от продавливания контролировать инструментально до бетонирования перекрытия. Проверке подлежит привязка к осям и граням колонн, ориентация, размеры, высотное положение, расстояния от граней колонн, взаимный шаг и надёжность закрепления. Результаты проверки зафиксировать в исполнительной документации и предъявить при освидетельствовании.

57. Проверка арматуры.

58. В процессе бетонирования стен, колонн и перекрытия контролировать документы на бетонную смесь, последовательность и непрерывность укладки, толщину укладываемых слоев, качество уплотнения, состояние опалубки и стоек, а также неизменность положения арматуры, закладных изделий, проходов и каркасов от продавливания. Обнаруженные смещения устранить до продолжения бетонирования соответствующего участка.

59. После распалубки стен, колонн и перекрытия проверить фактические геометрические размеры, положение осей и отметок, вертикальность стен и колонн, отметки поверхности перекрытия, качество бетонных поверхностей, отсутствие недопустимых раковин, пустот, обнажения арматуры, трещин и иных дефектов.

60. Контроль и участие работ, имеющих отклонения от рабочей документации по согласованному решению.

61. Приёмку ответственных конструкций выполнять в случаях и порядке, предусмотренных нормативными документами, рабочей документацией и ППР.

62. По завершении соответствующих этапов работ выполнять исполнительную геодезическую съёмку:

- стен и колонн — положение осей, граней, отметок и вертикальность;
- перекрытий — отметки поверхности, положение проёмов и контуров;
- закладных изделий, выпусков и иных элементов, положение которых подлежит геодезическому контролю.

63. Исполнительные геодезические схемы оформлять в соответствии с ГОСТ Р 51872-2004.

64. Конструкции и участки работ, имеющие отклонения от рабочей документации по согласованному решению, не подлежат контролю и выполнению работ до принятия согласованного технического решения.

65. По окончании работ передать Заказчику комплект исполнительной документации, включающий акты освидетельствования, акты приёмки ответственных конструкций, исполнительные схемы, журналы работ, документы о качестве материалов, протоколы контроля бетона и результаты геотехнического мониторинга.

66. Работы выполнять с соблюдением требований охраны труда, пожарной и экологической безопасности.

– стен и колонн — положение осей, граней, отметок и вертикальность;

– перекрытий — отметки поверхности, положение проёмов и контуров;

60. Исполнительные геодезические схемы оформлять в соответствии с ГОСТ Р 51872-2024

61. Конструкции и участки работ, имеющие отклонения от рабочей документации или повреждения, не допускается закрывать последующими работами до принятия согласованного технического решения.

62. По окончании работ передать Заказчику комплект исполнительной документации, включающий акты

освидетельствования, акты приемки ответственных конструкций, исполнительные схемы, журналы работ, документы о качестве материалов, протоколы контроля бетона и результаты геотехнического мониторинга.

63. Работы выполнять с соблюдением требований охраны труда, пожарной и экологической безопасности.

					260402082 - КЖ1-01			
					Лабораторно-производственный корпус, г. Москва, г. Зеленоград, проспект Генерала Алексеева, 505			
Изм.	Кол.уч.	Лист № док.	Подпись	Дата	Лабораторно-производственный корпус	Статус	Лист	Листов
Разработал		Коломач		02.09.26		Р	1	7
Проверил		Кирданов		02.09.26				
Н.контр.	Рыбальченко		02.09.26	Общие данные		 ПЭТРУСКО СИНТЕТИЧЕСКИЕ МАТЕРИАЛЫ		

Инв. № подл.	Подп. и дата	Взам. инв. №	Создано			







 **ПЭТРУСКО**
Строительство в интересах

Спецификация элементов колонны Км-1-1

Поз.	Обозначение	Наименование	Кол.	Масса ед, кг	Примечание
		<u>Детали</u>			
32-600	ГОСТ 34028-2016	Ø32 A500C L= 6000	12	37,86	454,32
10-X.41.41	ГОСТ 34028-2016	Ø10 A240 L= 1805	29	1,114	32,28
		<u>Изделия</u>			
Мф-1		Муфта обжимная d32	12	2,25 кг	см.п.3
		<u>Материалы</u>			
	ГОСТ 26633-2015	Бетон В30			1,44 м ³

Ведомость деталей


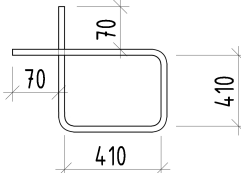
Поз.	Эскиз
10-Х.41.4.1	

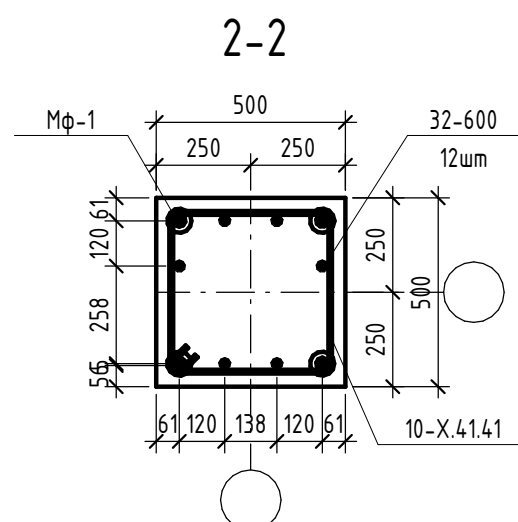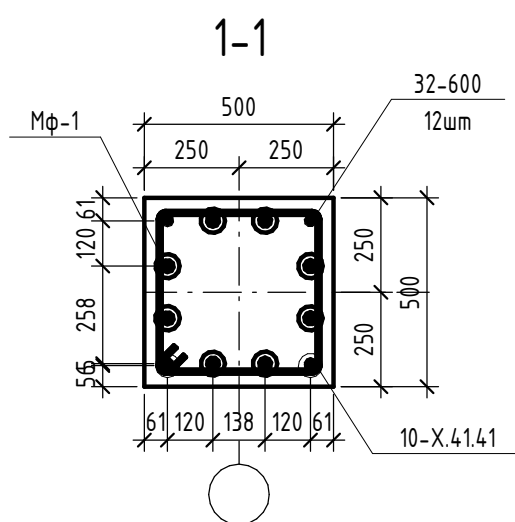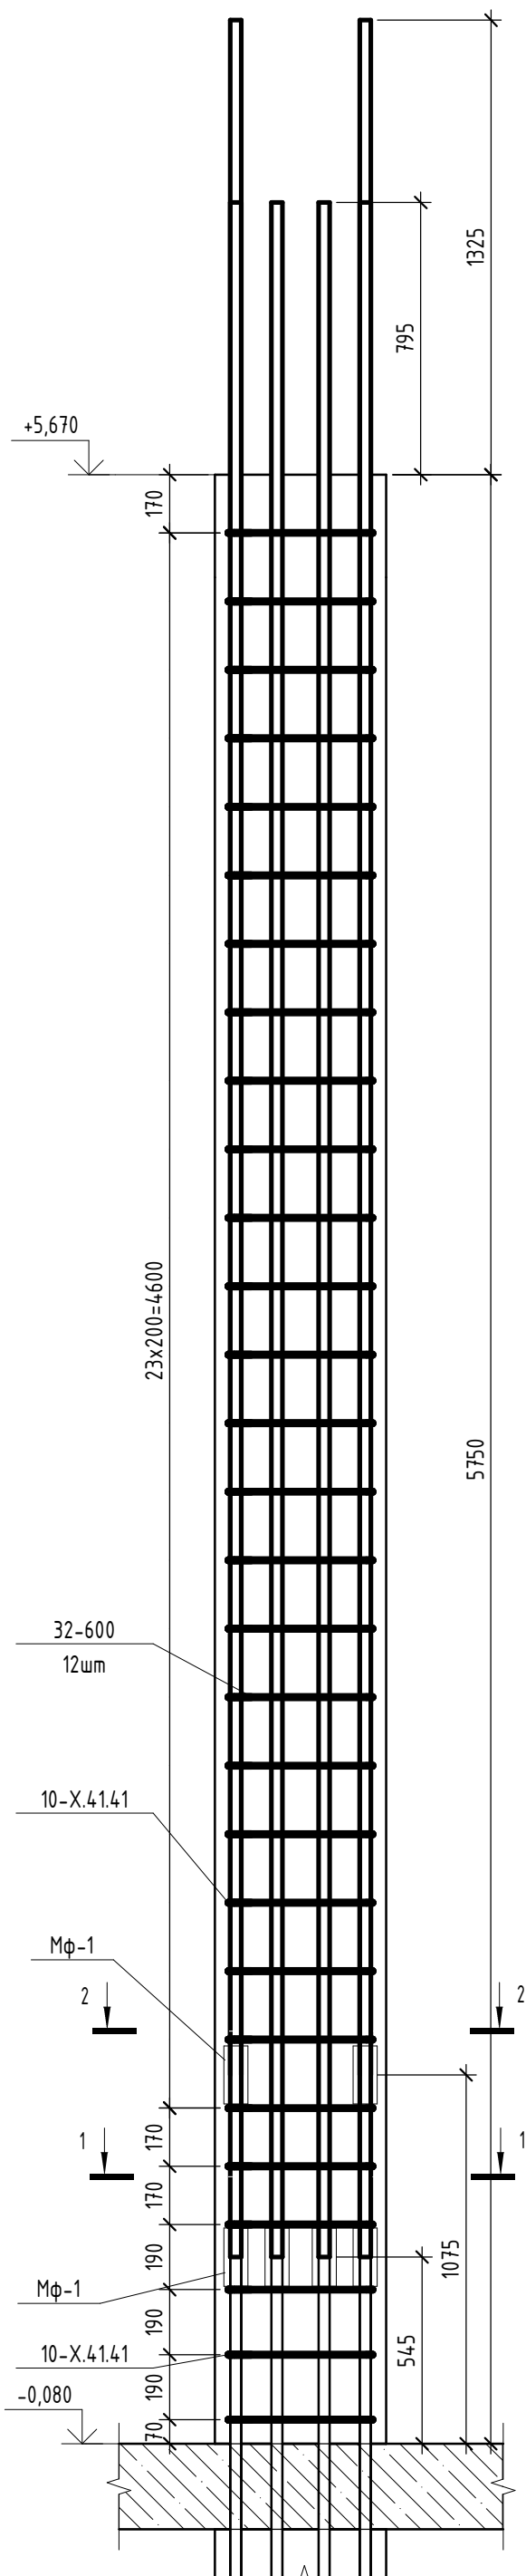

1. Общие указания, сводную ведомость расхода стали, бетона материалов см. лист 1.
2. Данный лист смотреть совместно с листом 2.
3. Соединительные муфты Мф-1 приняты по ТУ 4842-003-75604862-2012. Соединение выполнить путем опрессовки соединительных муфт с использованием гидравлической мобильной установки в построчечных условиях. Длина соединительной муфты до опрессовки, при диаметре соединяемой арматуры ф32 равна 192мм.

Инф. № подл.	Подп. и дата	Взам. инф. №	Согласовано		


						260402082 - КЖ1-3			
						Лабораторно-производственный корпус, г. Москва, г. Зеленоград, проспект Генерала Алексеева, 50Б			
Изм.	Кол.уч.	Лист	№ док.	Подпись	Дата		Стадия	Лист	Листов
Разработал	Алейников				02.09.26	Лабораторно-производственный корпус	Р	3	
Проверил	Курданов				02.09.26				
					02.09.26	Колонна монолитная железобетонная Км-1-1 на отм. -0,080		ПЭТРУСКО Строительство в медицине	
Н.контр.	Рыбальченко								

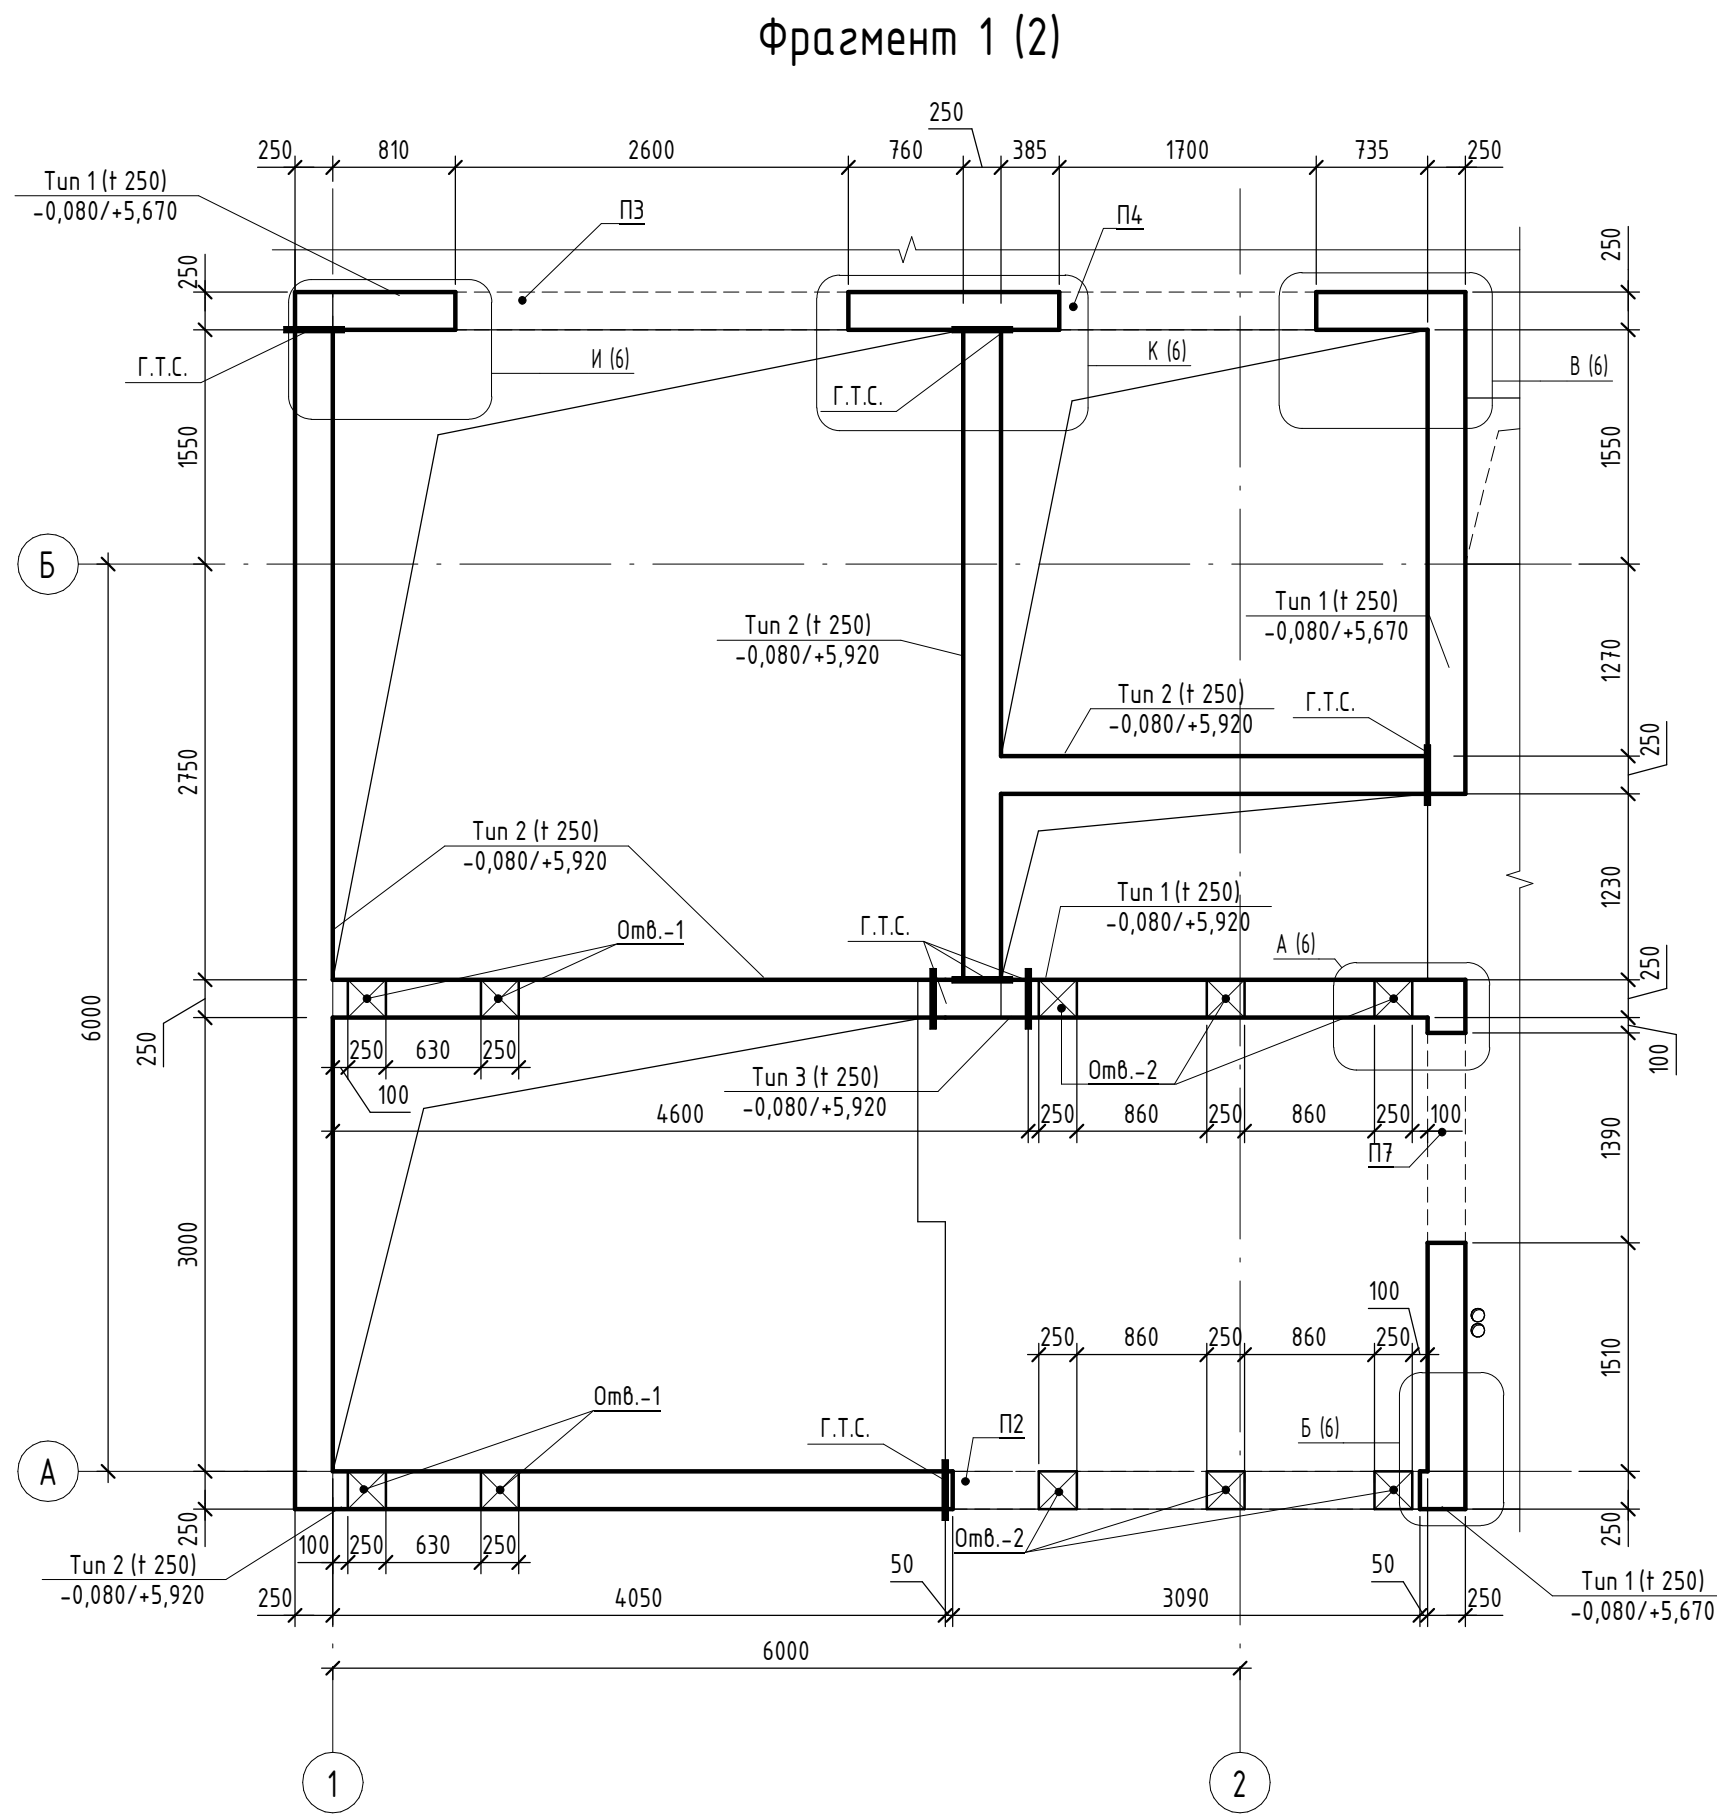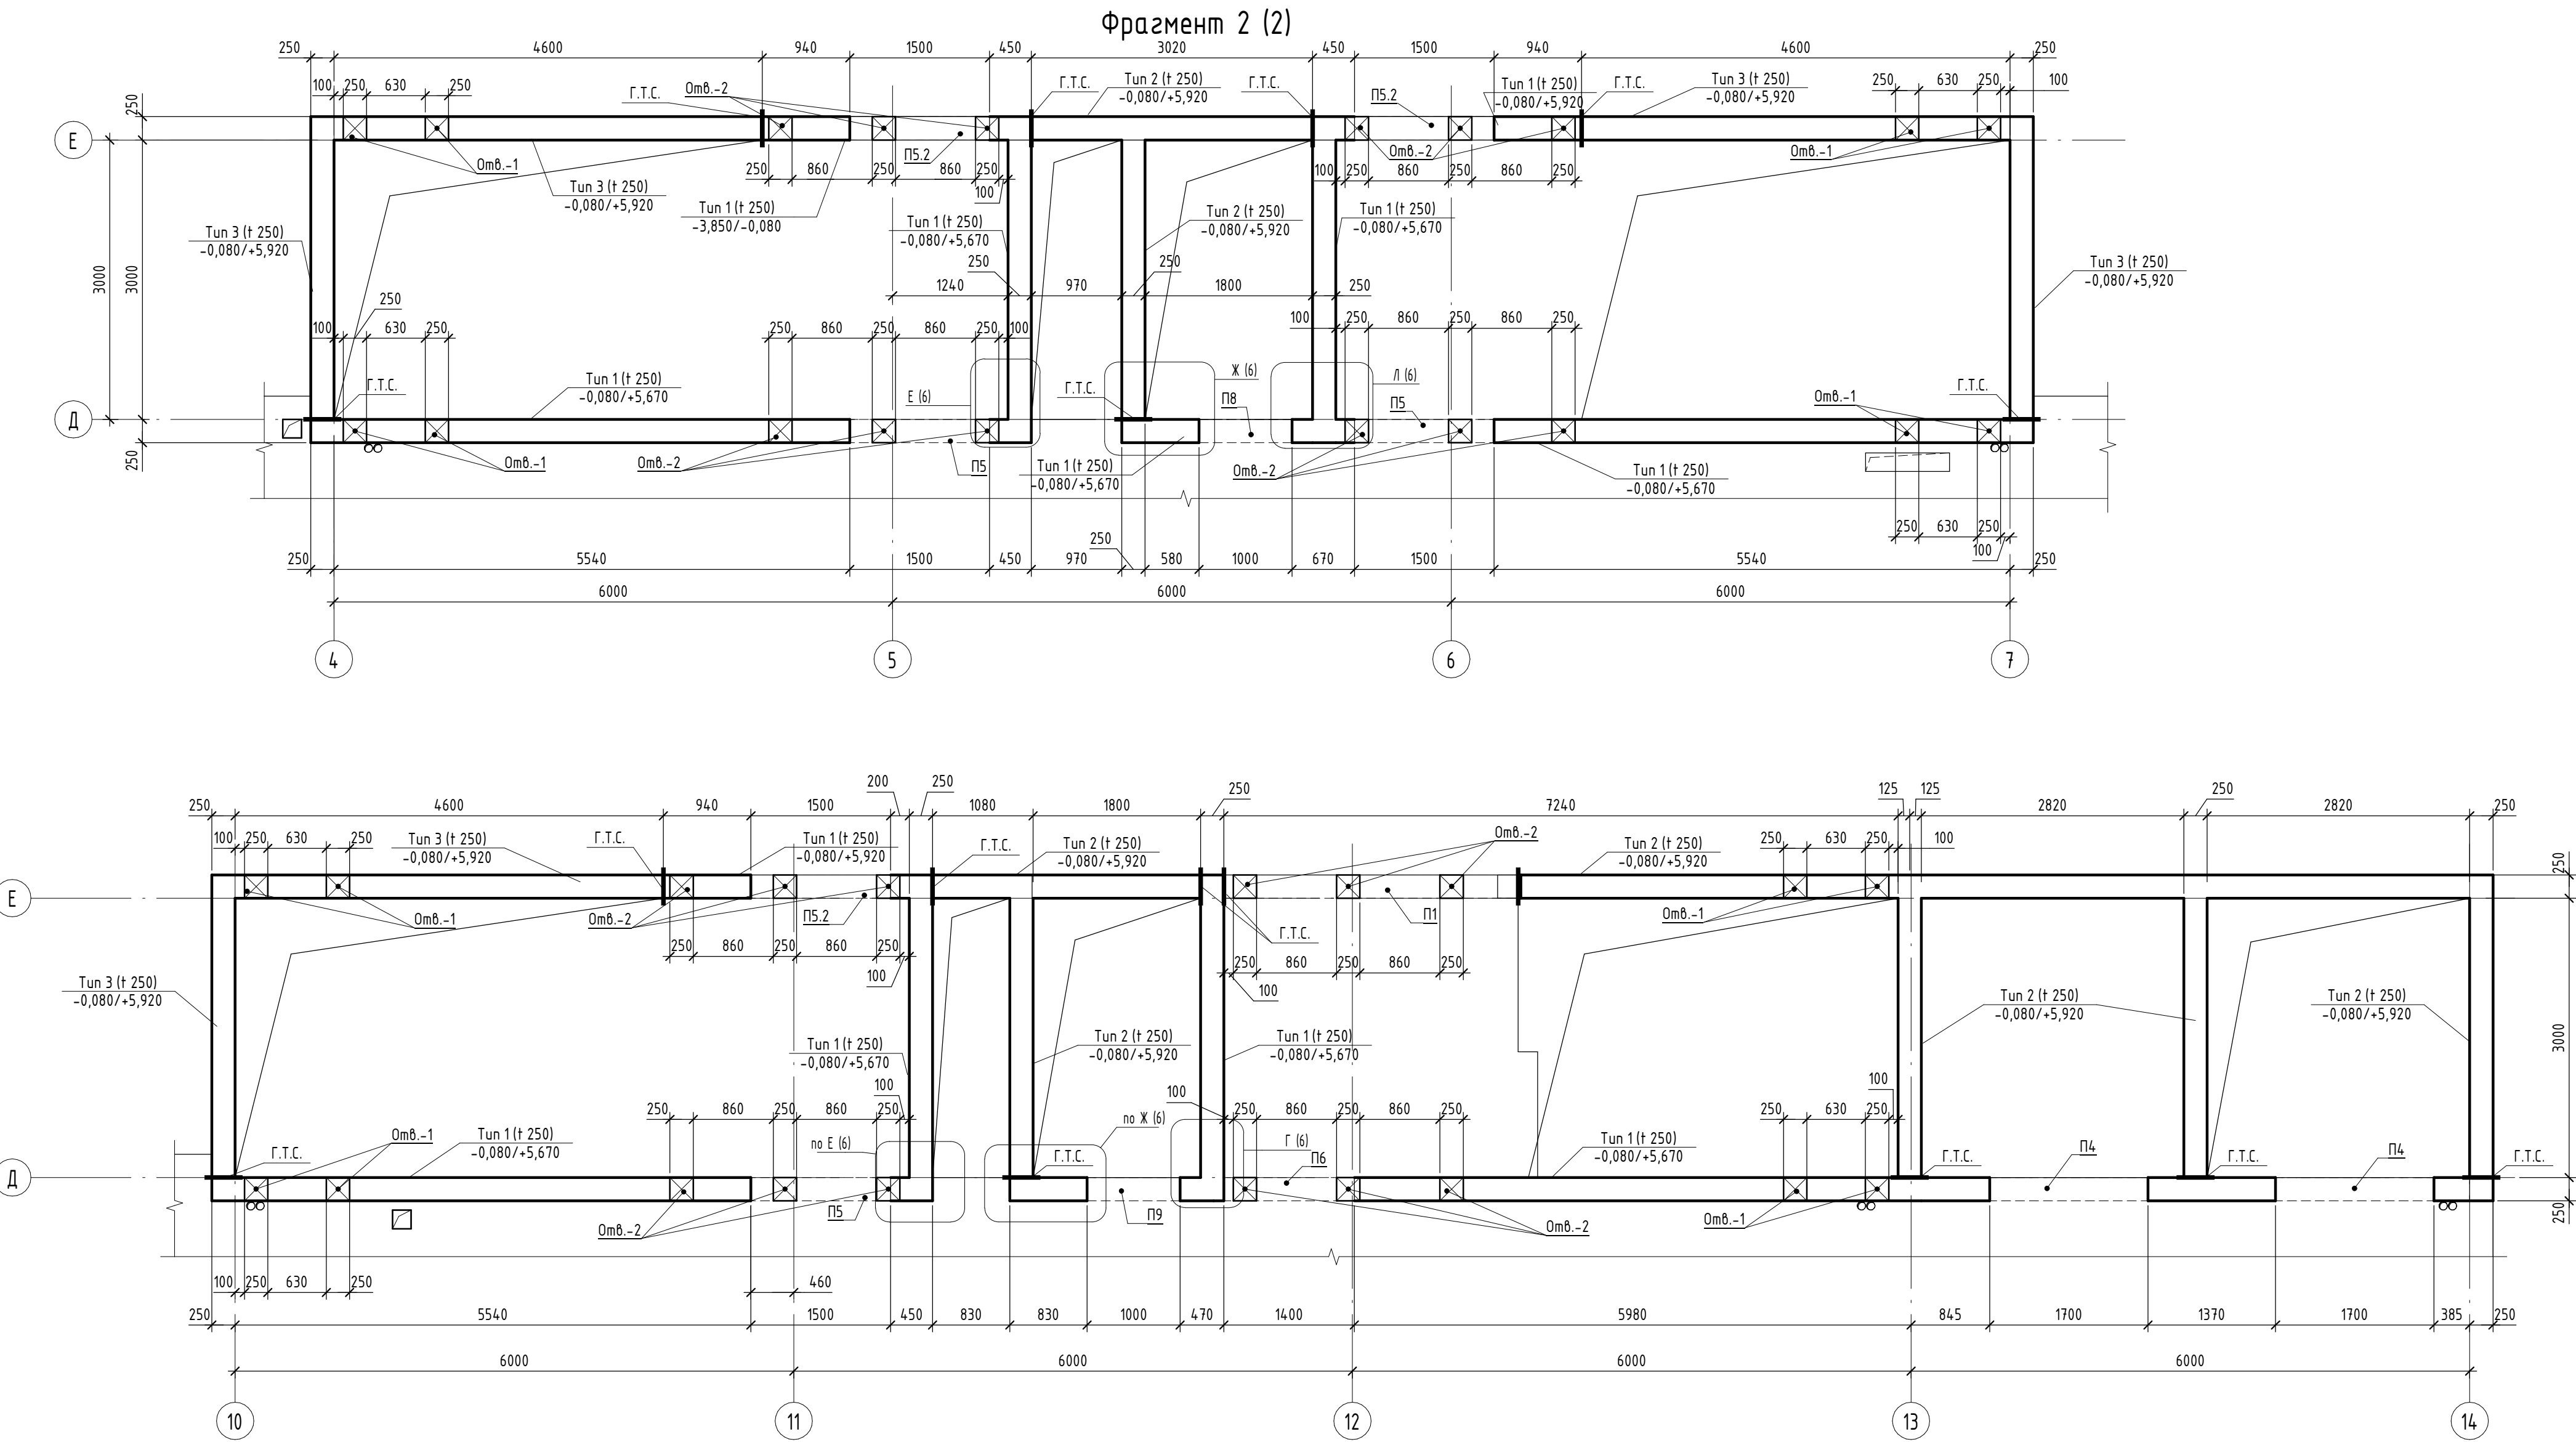

Ведомость проемов и отверстий

Марка отв.	Размеры, мм	Отм. низа проема, м	Назначение	Кол.	Примечание
Omb.-1	250x200(h)	+4,270		20	
Omb.-2	250x200(h)	+2,770		36	
Omb.-3	250x200(h)	+1,270		24	
П8	1000x2200(h)	отм. низа -0,080		1	
П9	1000x2200(h)	отм. низа -0,080		1	
П7	1390x2200(h)	отм. низа -0,080		1	
П6	1400x2200(h)	отм. низа -0,080		1	
П5	1500x2200(h)	отм. низа -0,080		4	
П5.2	1500x2200(h)	отм. низа -0,080		4	
П4	1700x2200(h)	отм. низа -0,080		4	
П3	2600x2200(h)	отм. низа -0,080		1	
П2	3090x2200(h)	отм. низа -0,080		1	
П1	3190x2200(h)	отм. низа -0,080		1	

Фрагмент 4 (2)







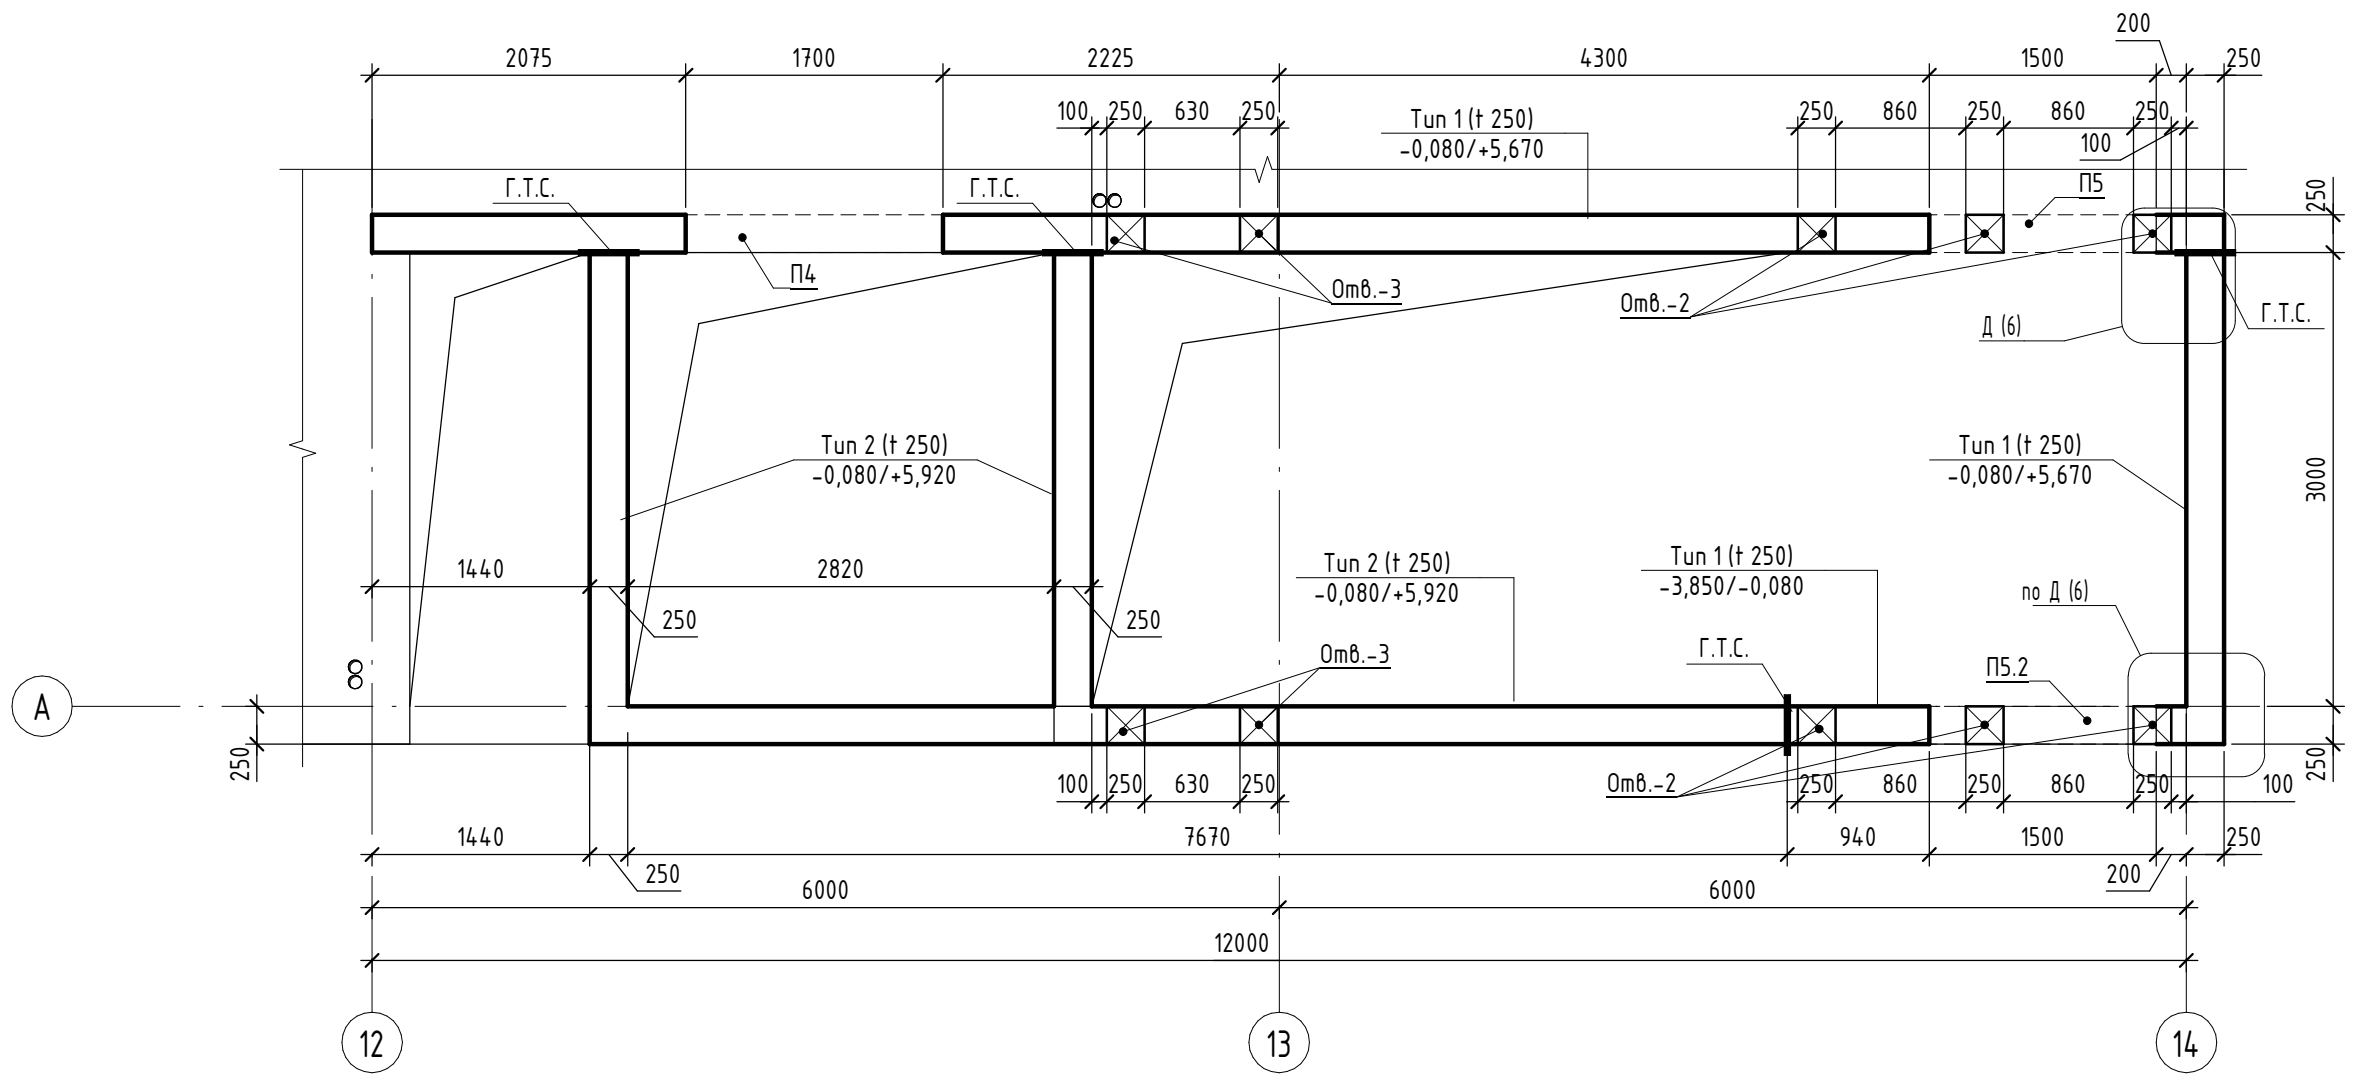


1. Общие указания см. лист 1

Условные обозначения:

- ~~~~~ - Рабочий шов бетонирования
- [-0,080] - Отметка верха и толщина плиты перекрытия
- t=250
- | - Г.Т.С. (граница типа стены)

260402082 - КЖ1-05					
Лабораторно-производственный корпус, г. Москва, г. Зеленоград, проспект Генерала Алексеева, 50Б					
Изм.	Колуч.	Лист	№ док.	Подпись	Дата
Разработал	Коломеев	02.09.26	02.09.26		
Проверил	Кирилов	02.09.26			
Н.контр.	Рыбальченко	02.09.26			
Лабораторно-производственный корпус				Стация	Лист
				Р	5
Фрагменты расположения вертикальных несущих конструкций на отм.-0,080. Опалубка				ПЭТРУСЬКО	

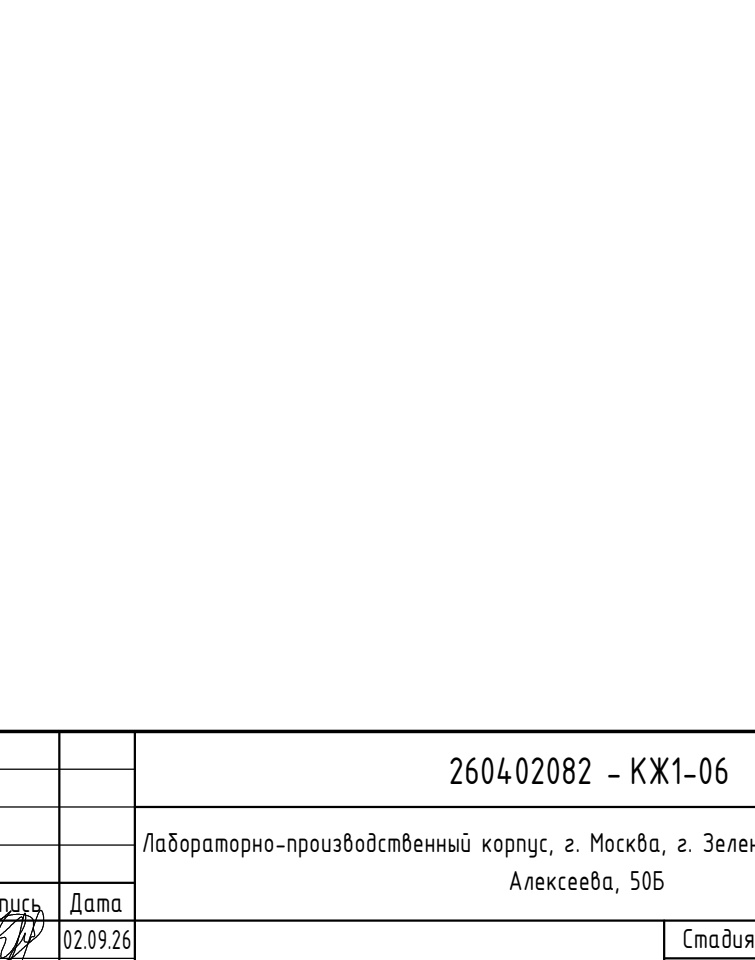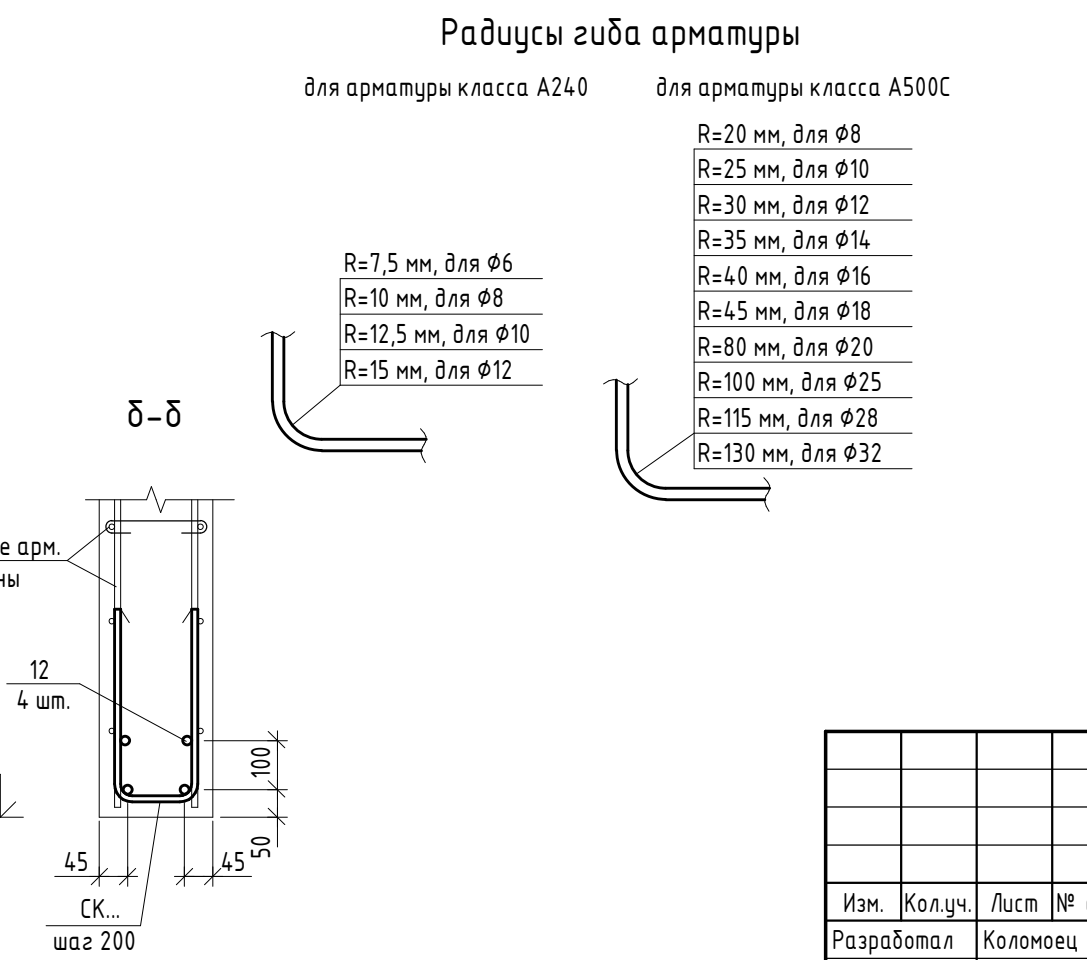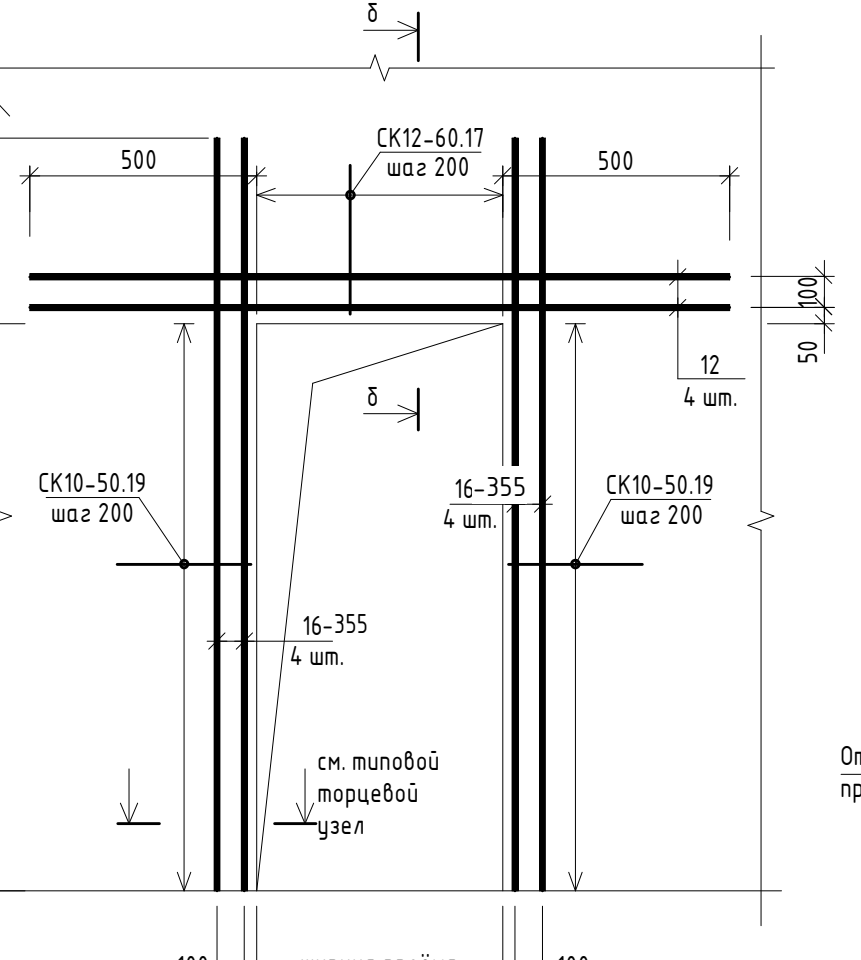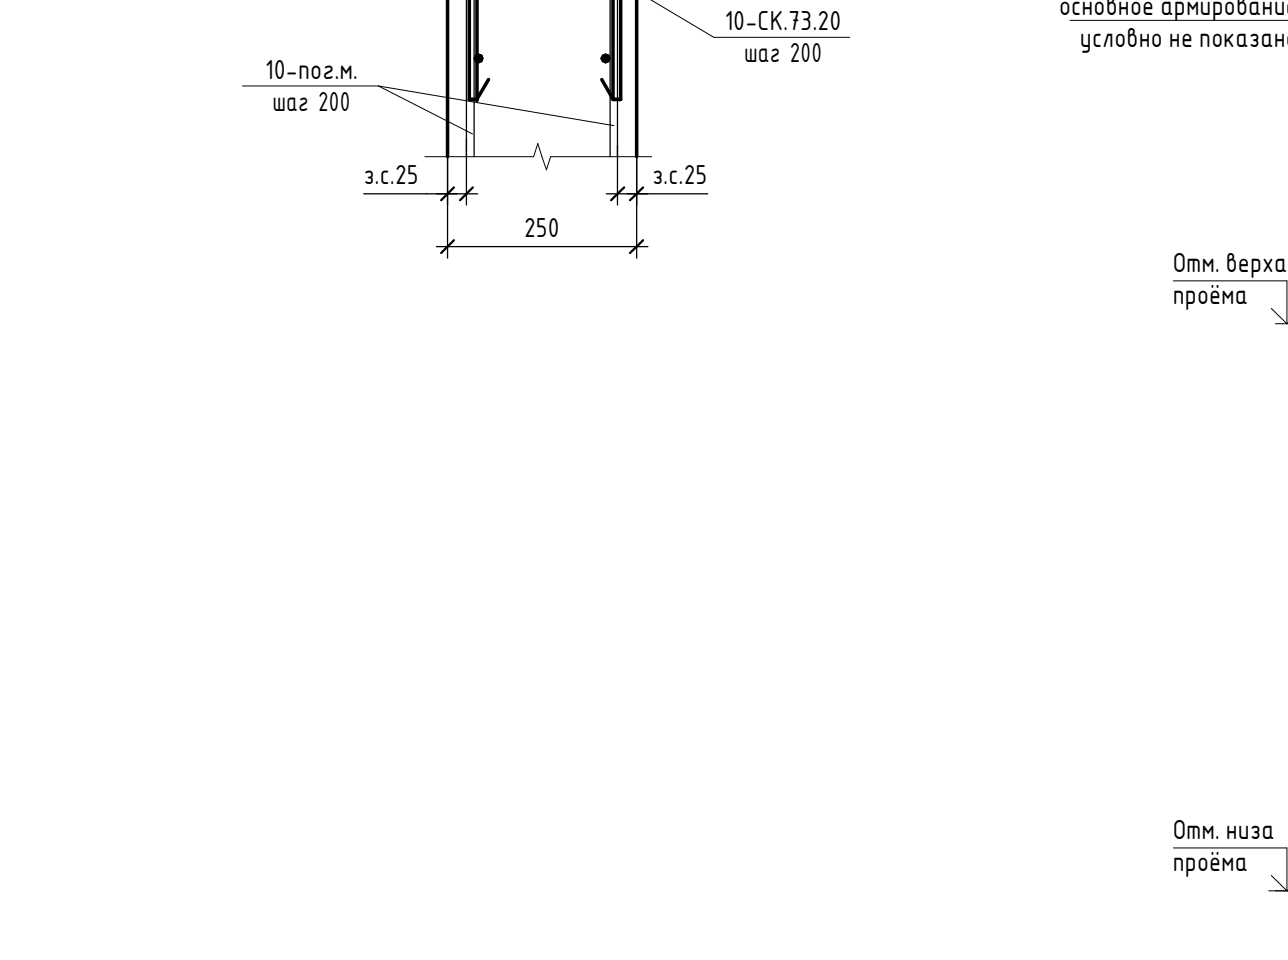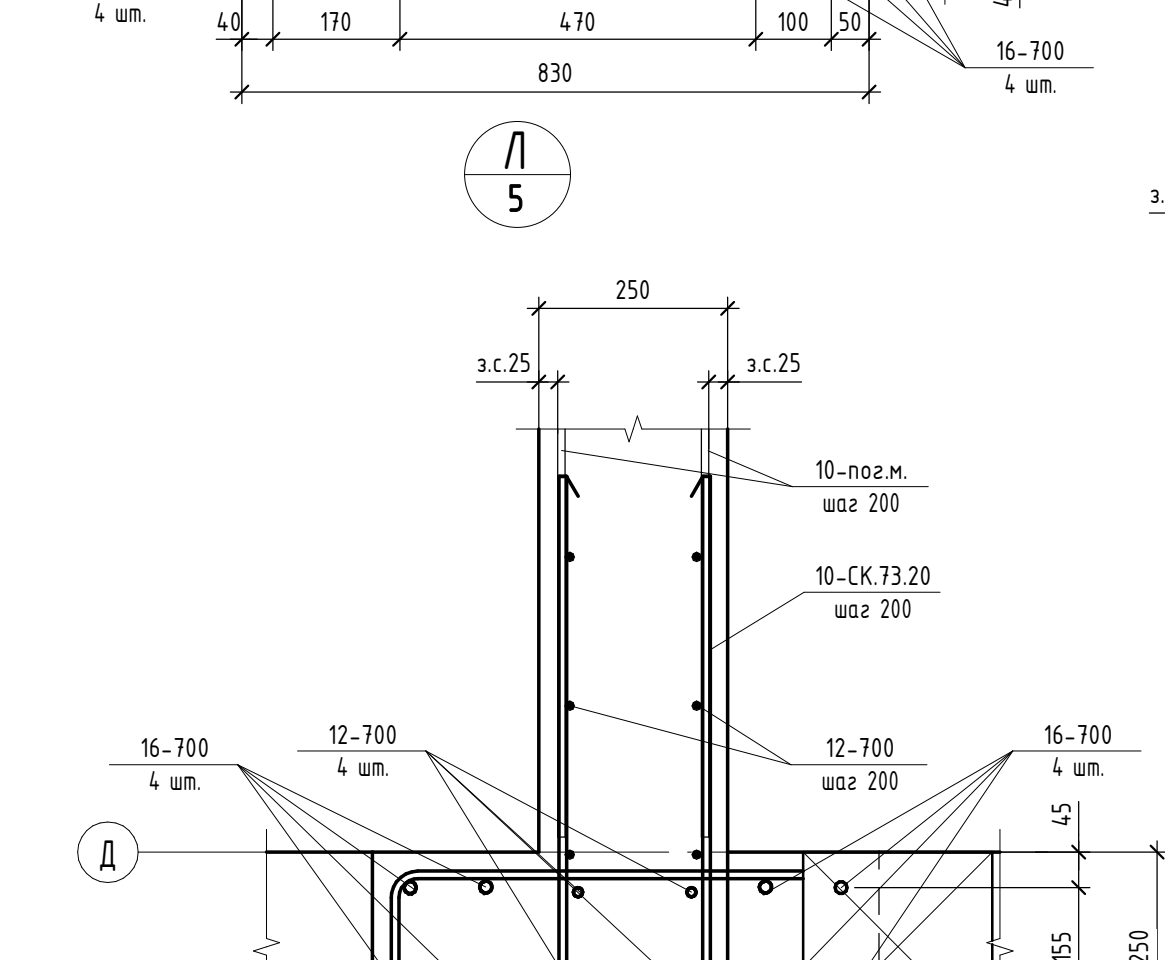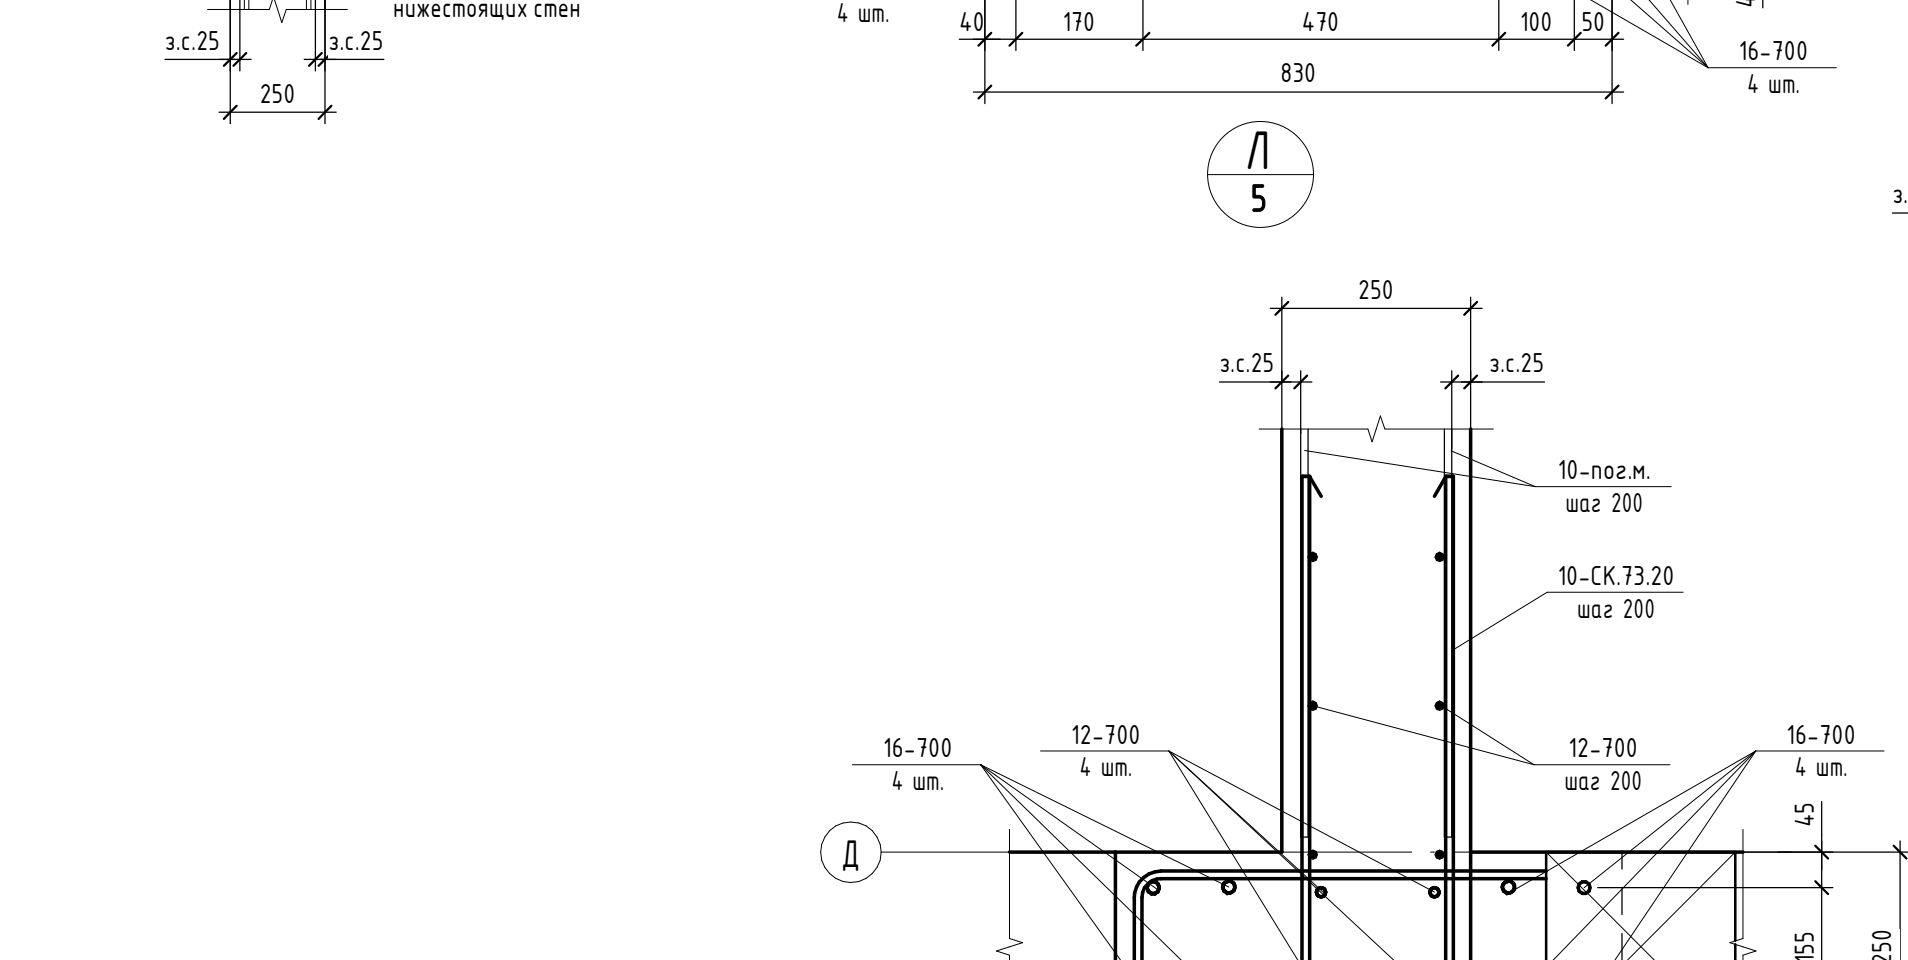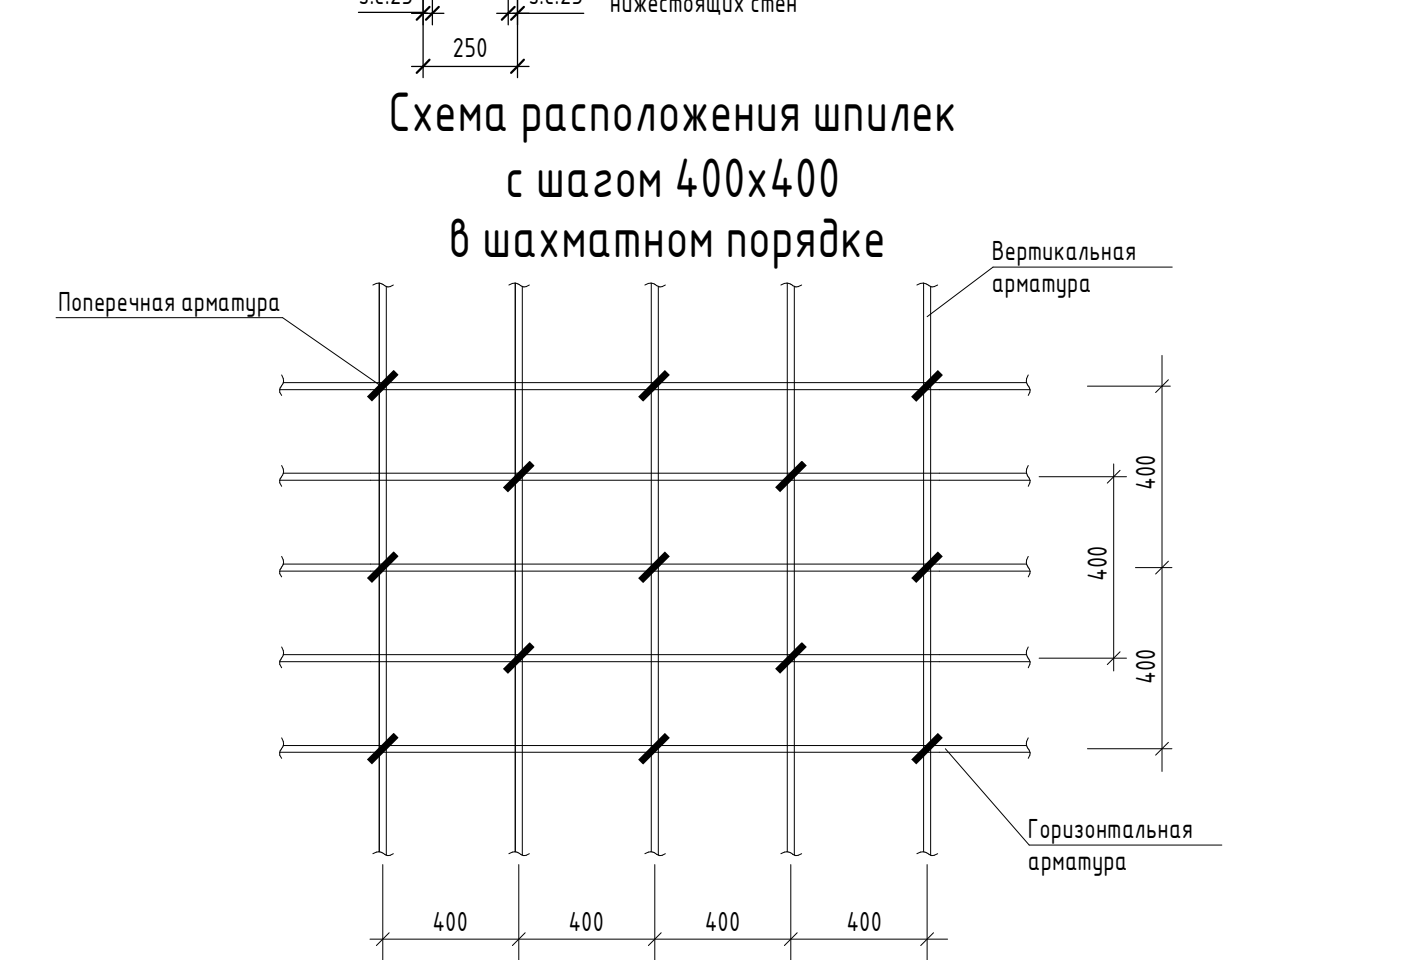

						2604 02082 - КЖ1-06					
						Лабораторно-производственный корпус, г. Москва, д. Зеленая, проспект Генерала Алексеева, 506					
Изм.	Кол-во	Лист	№ док.	Подпись	Дата	Лабораторно-производственный корпус			Страница	Лист	Листов
Разработана				<i>РП</i>	02.09.26				Р	6	
Проверена					02.09.26						
Нкомпр.				<i>СМ</i>	02.09.26	Узлы армирования, типы армирования вертикальных несущих конструкций на отм. -0,080			 ПЭТРУСКО ПРОЕКТИРОВАНИЕ И СТРОИТЕЛЬСТВО		


Спецификация арматуры стен на отм. -0,080						
Поз.	Обозначение	Наименование	Кол.	Масса ед, кг	Примечание	
		Детали				
10-поз.м.	ГОСТ 34028-2016	Ø10 A500C L, поз.м	11407,2	0,617	7038,22	
12-700	ГОСТ 34028-2016	Ø12 A500C L= 7000	1682	6,216	10456,04	
12-675	ГОСТ 34028-2016	Ø12 A500C L= 6750	54	5,994	323,60	
12-544	ГОСТ 34028-2016	Ø12 A500C L= 5440	10	4,831	48,30	
12-475	ГОСТ 34028-2016	Ø12 A500C L= 4750	306	4,218	1290,70	
12-394	ГОСТ 34028-2016	Ø12 A500C L= 3940	68	3,499	238,00	
12-360	ГОСТ 34028-2016	Ø12 A500C L= 3600	4	3,197	12,80	
12-284	ГОСТ 34028-2016	Ø12 A500C L= 2840	40	2,522	100,80	
12-278	ГОСТ 34028-2016	Ø12 A500C L= 2780	42	2,469	103,74	
12-270	ГОСТ 34028-2016	Ø12 A500C L= 2700	16	2,398	38,40	
12-250	ГОСТ 34028-2016	Ø12 A500C L= 2500	20	2,22	44,40	
12-244	ГОСТ 34028-2016	Ø12 A500C L= 2440	42	2,167	91,04	
12-240	ГОСТ 34028-2016	Ø12 A500C L= 2400	16	2,132	34,08	
12-219	ГОСТ 34028-2016	Ø12 A500C L= 2190	4	1,945	7,80	
12-200	ГОСТ 34028-2016	Ø12 A500C L= 2000	8	1,776	14,24	
12-134	ГОСТ 34028-2016	Ø12 A500C L= 1340	52	1,19	61,88	
12-59	ГОСТ 34028-2016	Ø12 A500C L= 590	28	0,524	14,60	
16-700	ГОСТ 34028-2016	Ø16 A500C L= 7000	104	11,046	1149,20	
16-439	ГОСТ 34028-2016	Ø16 A500C L= 4390	6	6,928	41,58	
16-407	ГОСТ 34028-2016	Ø16 A500C L= 4070	4	6,423	25,68	
16-355	ГОСТ 34028-2016	Ø16 A500C L= 3550	48	5,602	268,80	
10-СК.73.20	ГОСТ 34028-2016	Ø10 A500C L= 1615	539	0,997	539,00	
10-СК.73.20	ГОСТ 34028-2016	Ø10 A500C L= 1605	1516	0,991	1500,84	
10-СК.50.20	ГОСТ 34028-2016	Ø10 A500C L= 1155	30	0,713	21,30	
10-СК.50.19	ГОСТ 34028-2016	Ø10 A500C L= 1150	216	0,71	153,36	
10-СК.50.19	ГОСТ 34028-2016	Ø10 A500C L= 1140	36	0,704	25,20	
12-СК.60.17	ГОСТ 34028-2016	Ø12 A500C L= 1320	137	1,173	160,29	
12-СК.60.17	ГОСТ 34028-2016	Ø12 A500C L= 1310	32	1,164	37,12	
10-Х.133.18	ГОСТ 34028-2016	Ø10 A500C L= 3220	12	1,987	23,88	
10-Х.100.18	ГОСТ 34028-2016	Ø10 A500C L= 2570	11	1,586	17,49	
10-Х.93.18	ГОСТ 34028-2016	Ø10 A500C L= 2420	11	1,494	16,39	
10-Х.77.18	ГОСТ 34028-2016	Ø10 A500C L= 2110	22	1,302	28,60	
10-Х.60.18	ГОСТ 34028-2016	Ø10 A500C L= 1770	12	1,093	13,08	
10-Х.58.18	ГОСТ 34028-2016	Ø10 A500C L= 1730	11	1,068	11,77	
10-Х.40.18	ГОСТ 34028-2016	Ø10 A500C L= 1370	12	0,846	10,20	
10-Х.39.18	ГОСТ 34028-2016	Ø10 A500C L= 1350	44	0,833	36,52	
10-Х.29.18	ГОСТ 34028-2016	Ø10 A500C L= 1150	11	0,71	7,81	
10-Х.24.18	ГОСТ 34028-2016	Ø10 A500C L= 1050	11	0,648	7,15	
8-Ш.19.6	ГОСТ 34028-2016	Ø8 A240 L= 310	14082	0,123	1732,09	

Поз.	Эскиз
10-СК.73.20	
10-СК.73.20	
10-СК.50.20	
10-СК.50.19	
10-СК.50.19	
12-СК.60.17	
12-СК.60.17	
10-Х.133.18	
10-Х.100.18	


Поз.	Эскиз
10-Х.93.18	
10-Х.77.18	
10-Х.60.18	
10-Х.58.18	
10-Х.40.18	
10-Х.39.18	
10-Х.29.18	
10-Х.24.18	
8-Ш.19.6	

Маркировка позиций арматуры


Фоновое армирование:

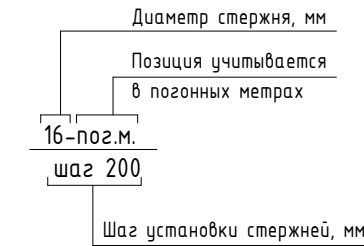

Прямые стержни:

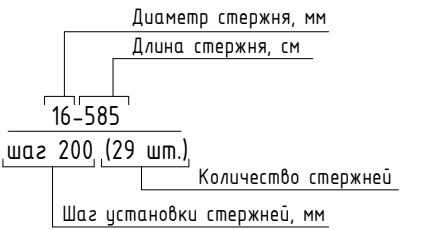

Гнутые детали:

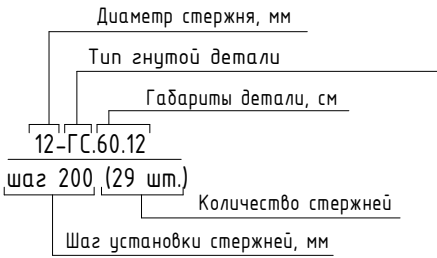

1. Данный лист смотреть совместно с листами 2..6

							260402082 - КЖ1-07
							Лабораторно-производственный корпус, г. Москва, г. Зеленоград, проспект Генерала Алексеева, 50Б
Изм.	Кол.уч.	Лист	№ док.	Подпись	Дата		
Разработал	Коломеец				02.09.26		
Проверил	Курданов				02.09.26	Лабораторно-производственный корпус	Стадия Р
Н.контр.	Рыбальченко				02.09.26	Спецификация арматуры стен на отм.-0,080. Водомость деталей	Лист 7
							Листов

